
2栋1户型 | CAD原始线稿

从DWG本地转换；文件单位：mm。保留原图几何，未补画隔墙。

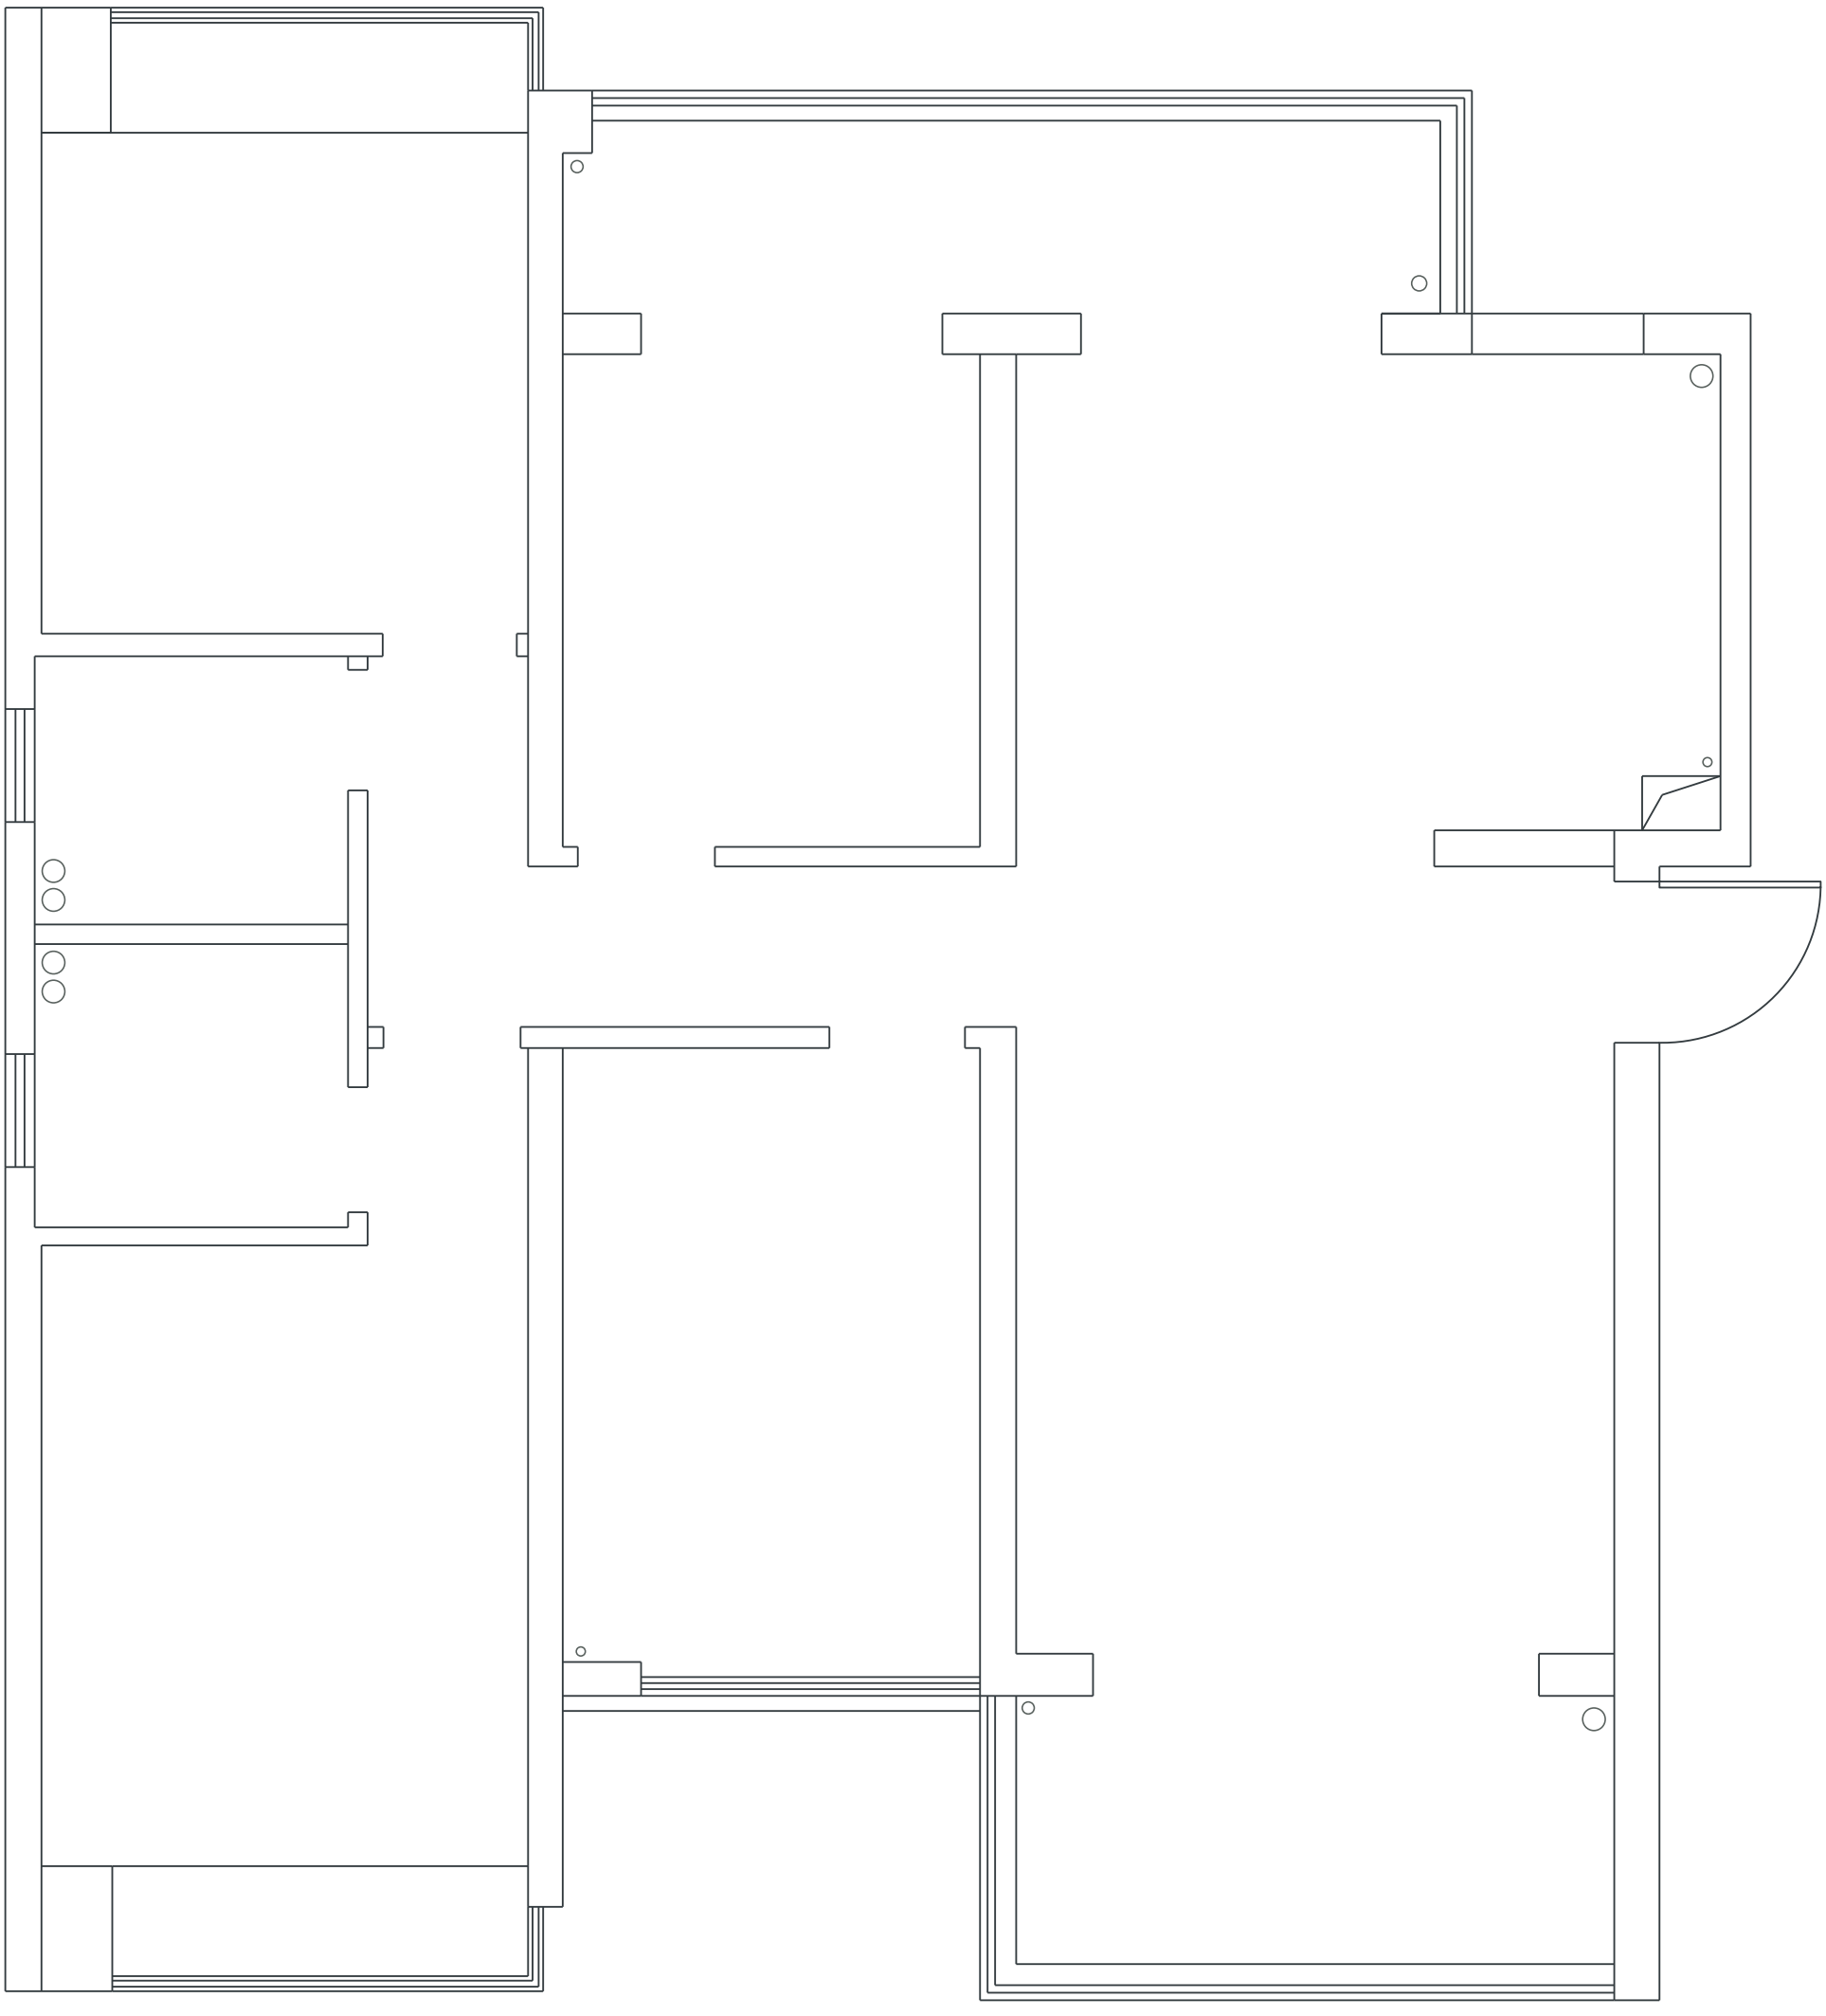


原文件未包含房间名称、尺寸标注或明确的墙体性质分层。

线稿范围约12050×13225mm，包含入户门开启线、飘窗等，不代表室内净尺寸。

2栋1户型 | 主要墙线净距核对

尺寸从CAD几何量取，单位mm，尚未现场复尺；房间名称依照片对应添加。

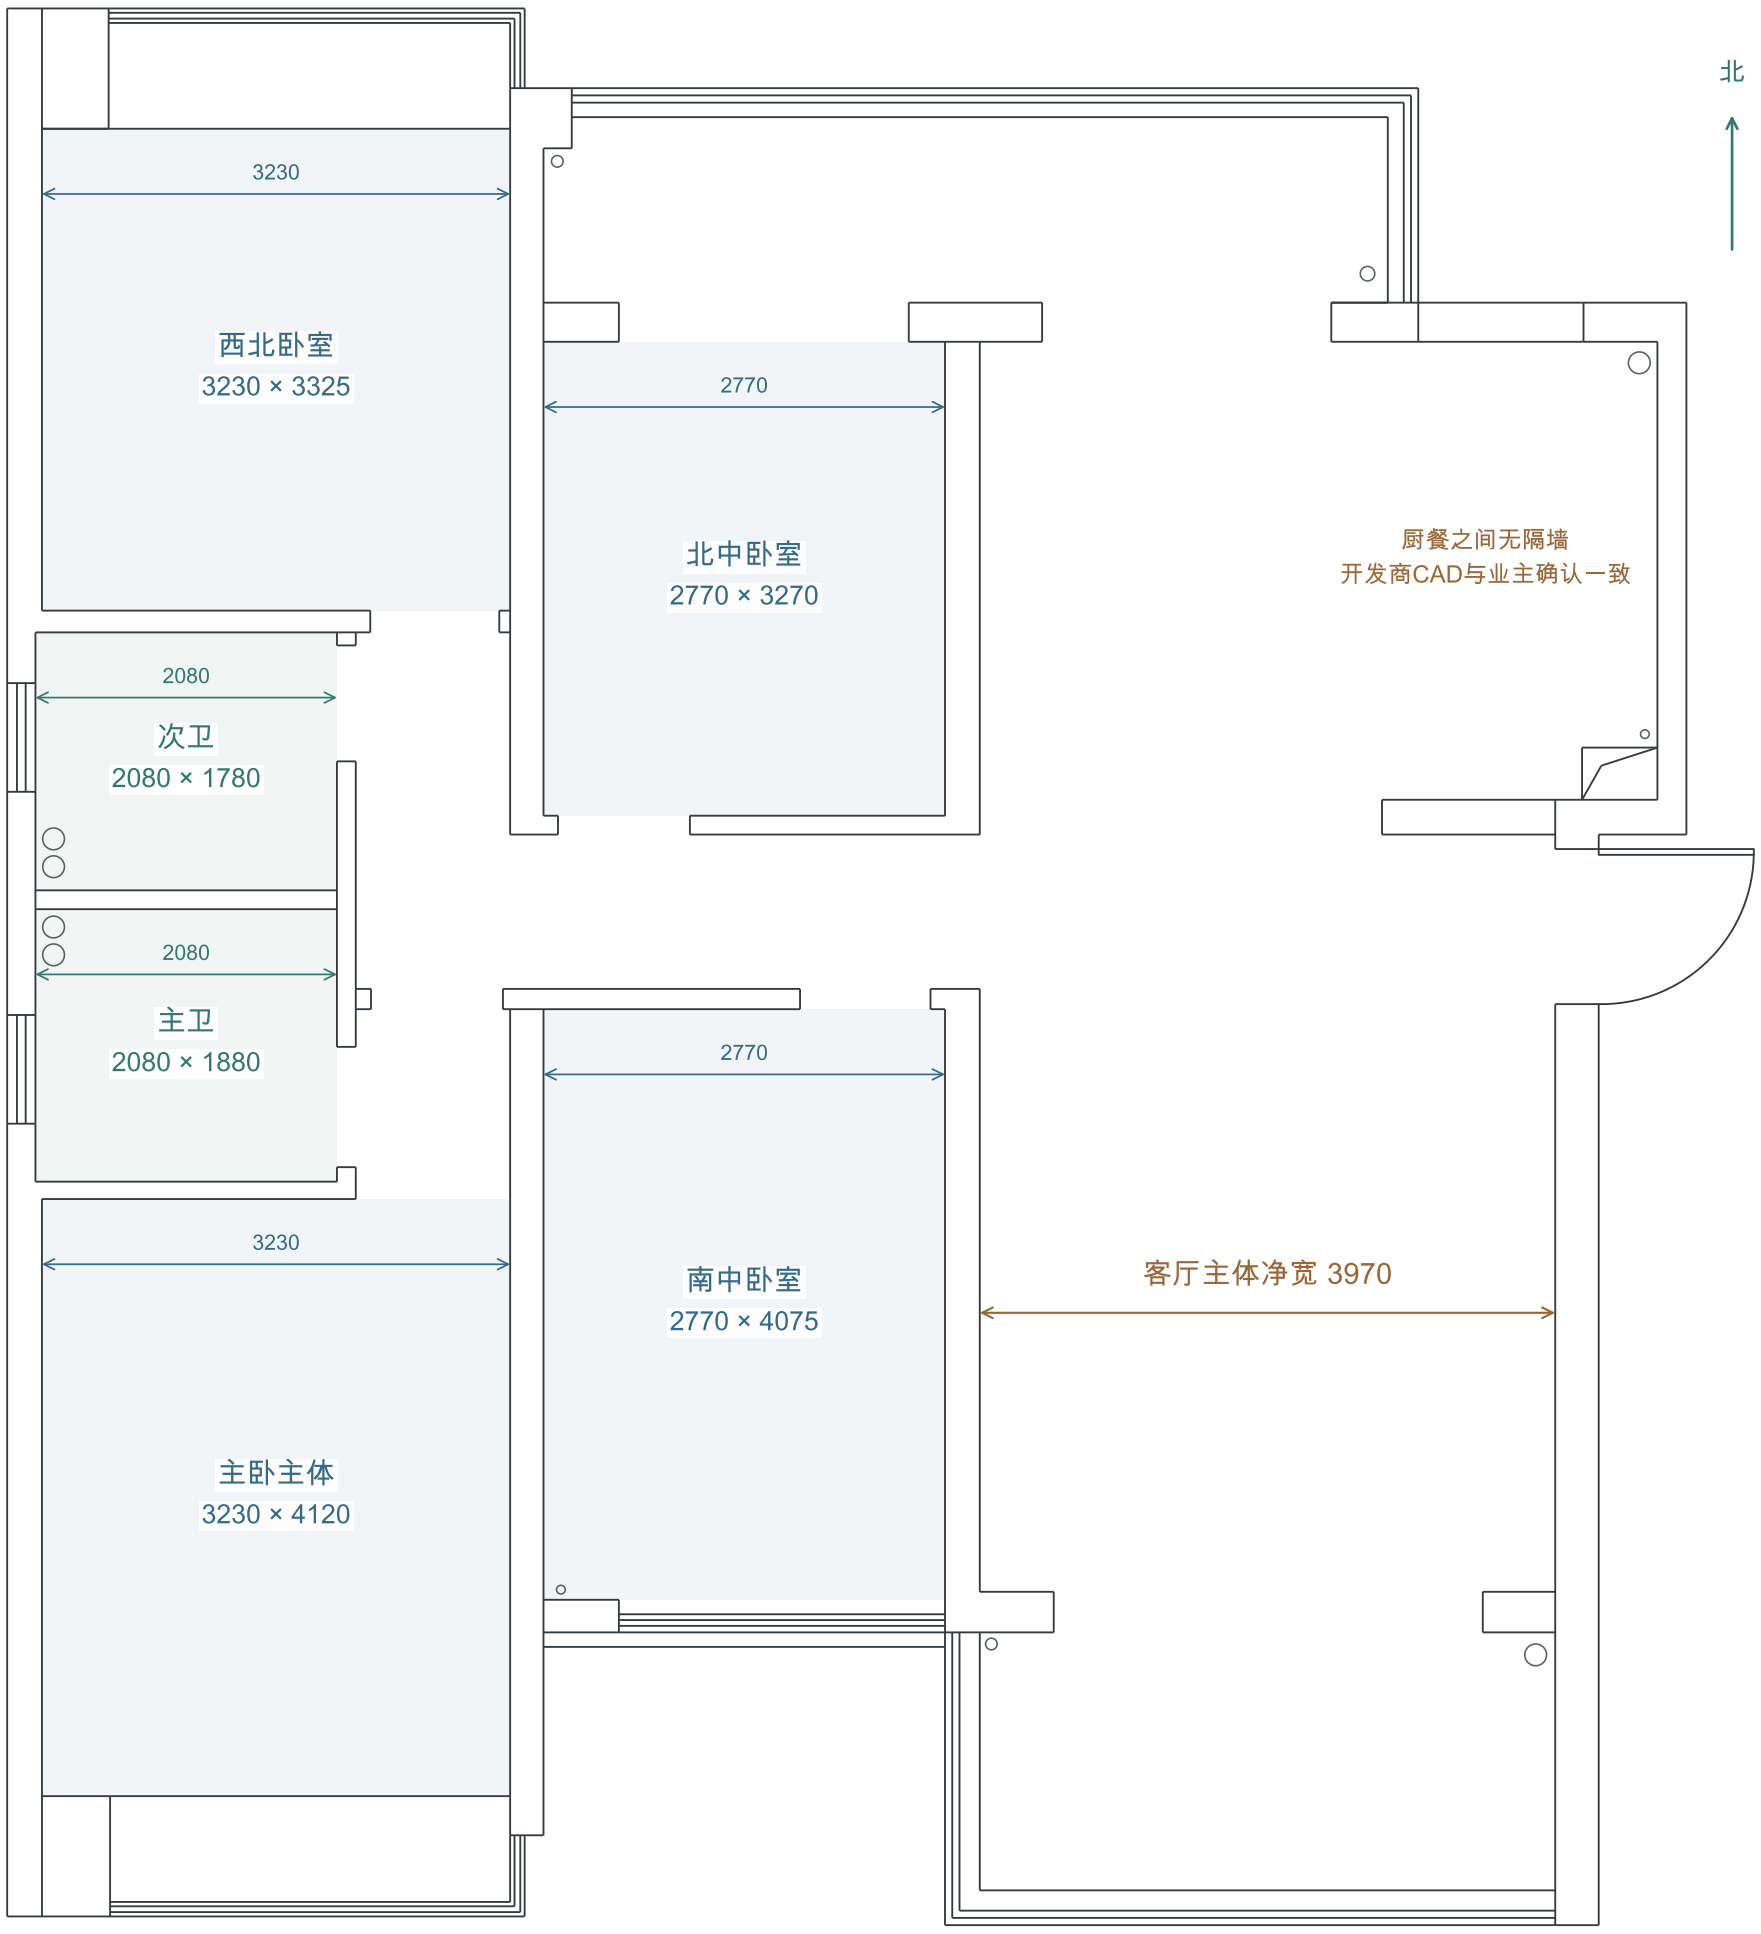

关键变化：手写3500对应两间左卧的主体净宽约3230；手写3000对应两间中卧净宽约2770。

客厅主体净宽约3970；南中卧的主体进深约4075，需据此校正照片模型。

北中卧北侧有开口；南中卧窗边有局部退入。上述长宽不用于直接认定整间房面积。

厨房与餐厅之间无隔墙已确认，不能继续沿用宣传图中的厨房西侧隔墙或自行补设门洞。

墙厚并不统一，图中可量到130、140、150、230、240、300mm等；线宽不代表承重性质。

层高2.9m、图上方朝北由业主提供。烟道、给排水、燃气及墙体性质仍需专项资料/现场核对。